


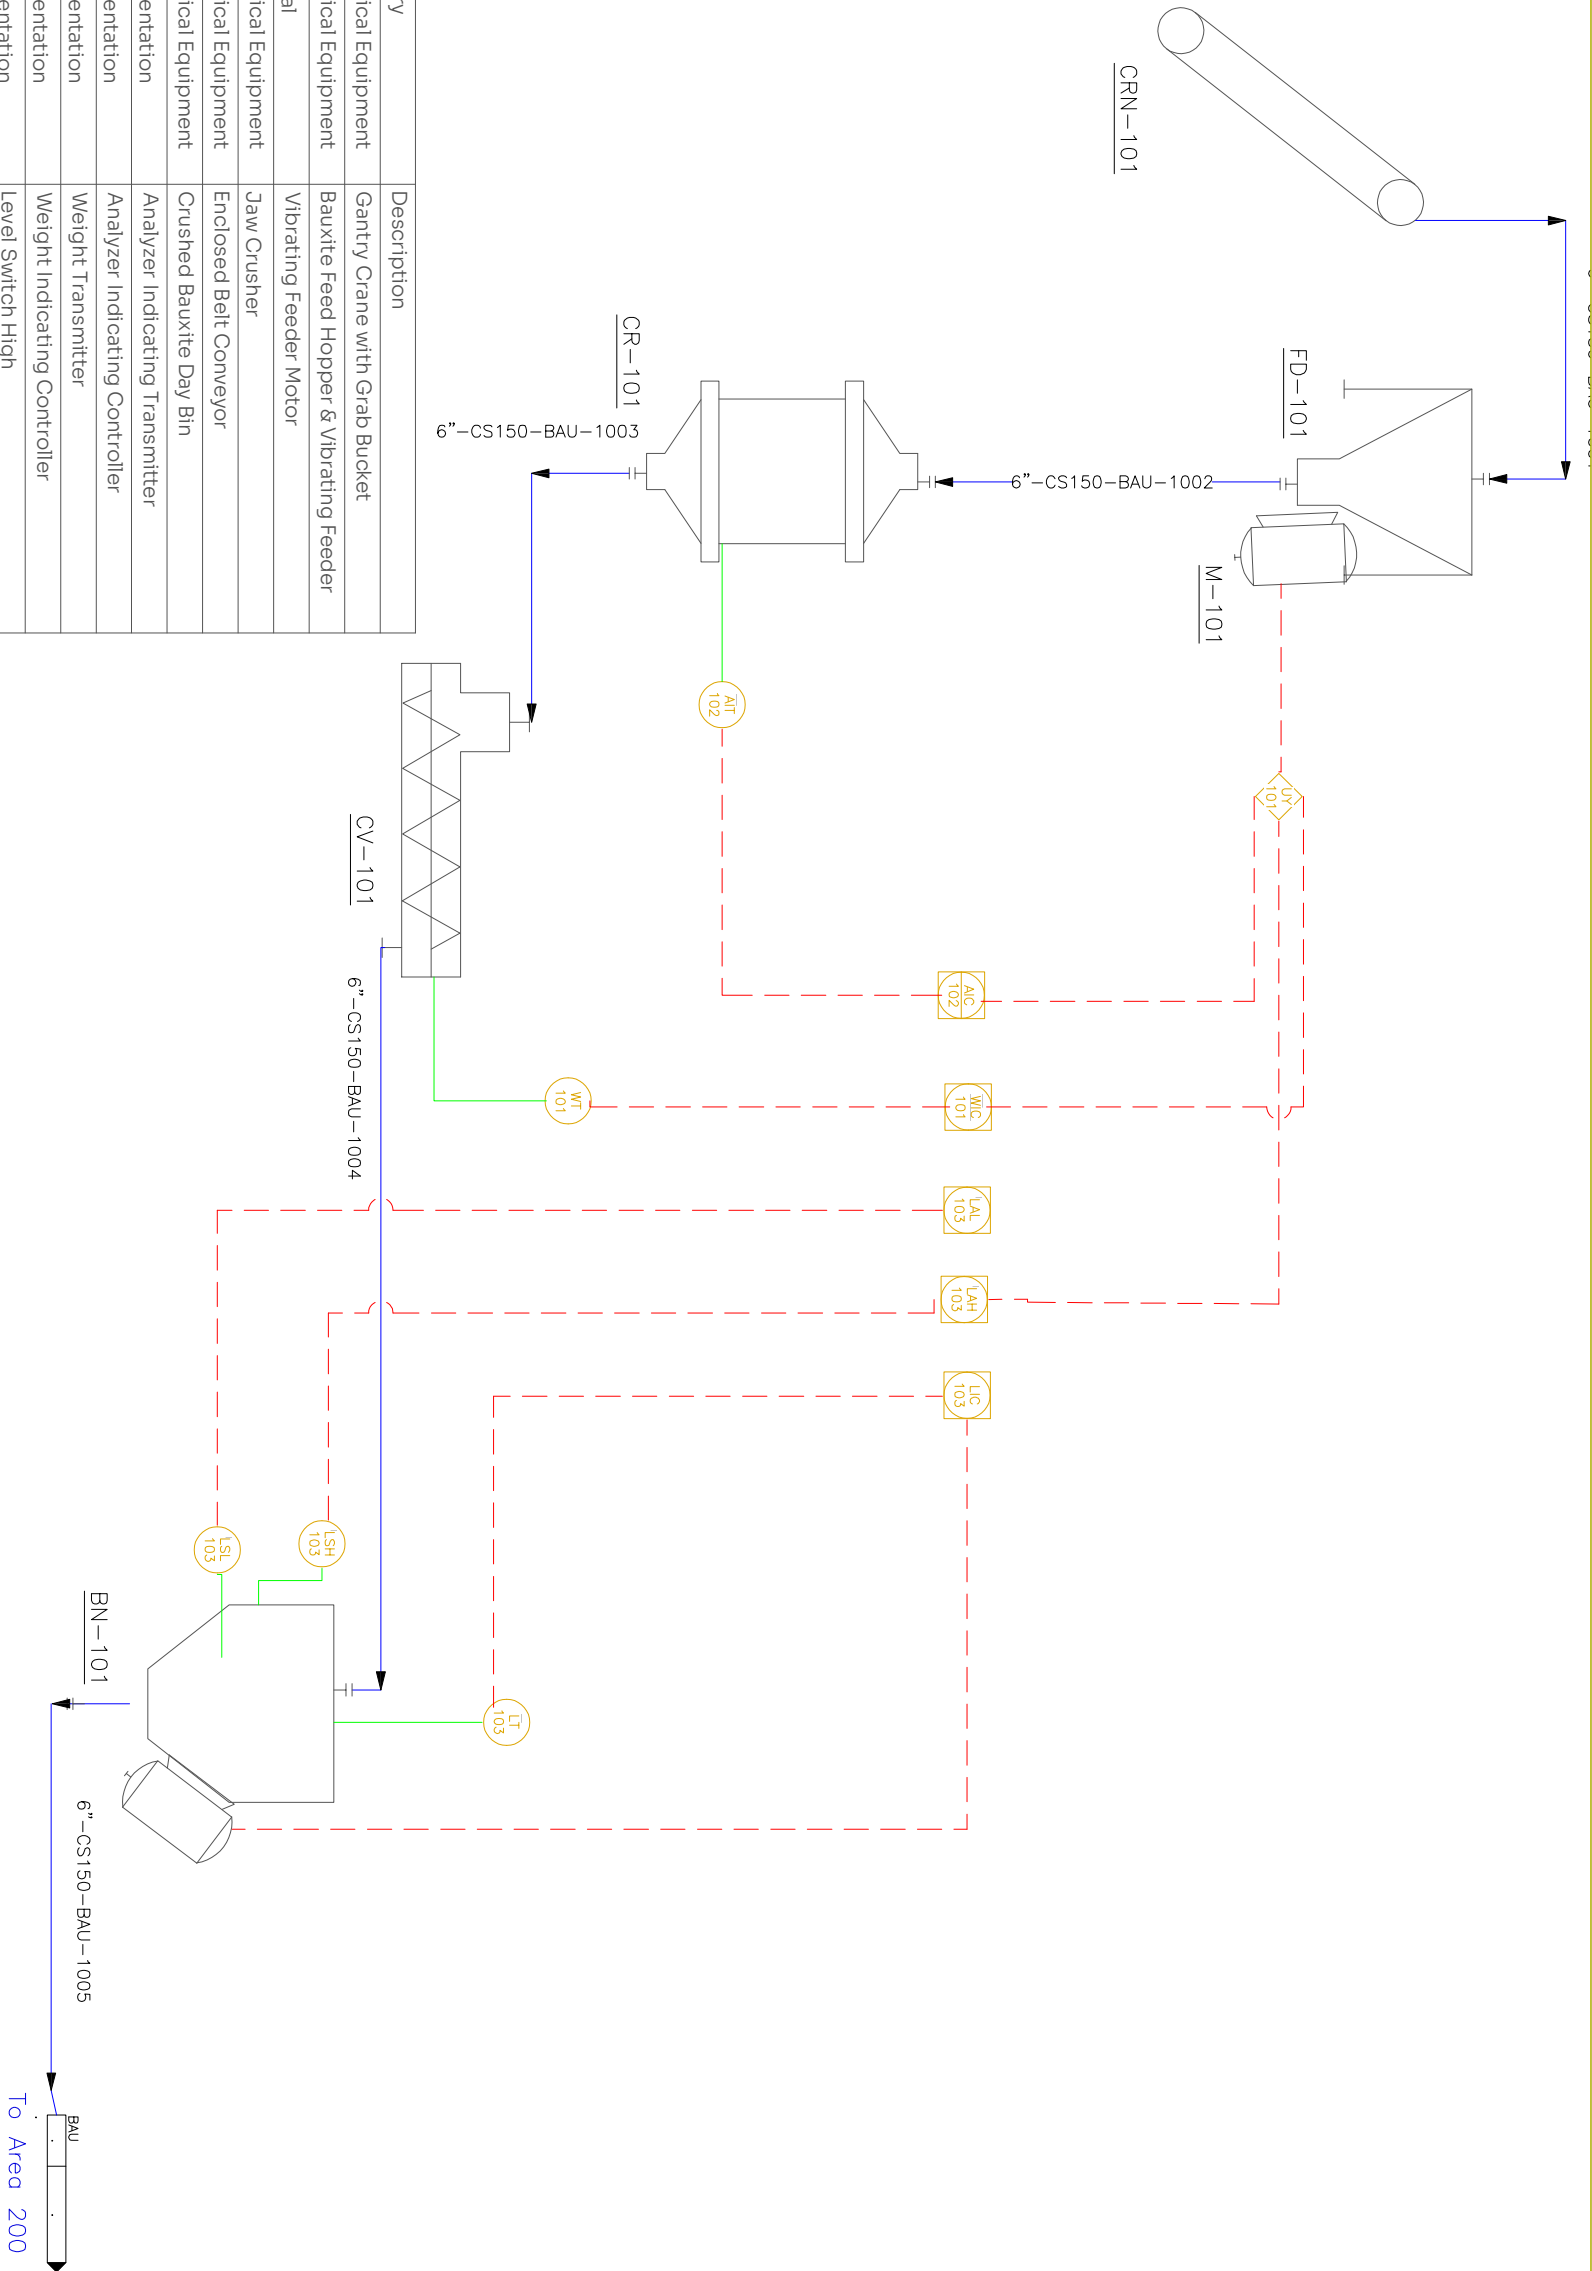

Tag Number	Category	Description
CRN-101	Mechanical Equipment	Gantry Crane with Grab Bucket
FD-101	Mechanical Equipment	Bauxite Feed Hopper & Vibrating Feeder
M-101	Electrical	Vibrating Feeder Motor
CR-101	Mechanical Equipment	Jaw Crusher
CV-101	Mechanical Equipment	Enclosed Belt Conveyor
BN-101	Mechanical Equipment	Crushed Bauxite Day Bin
AIT-102	Instrumentation	Analyzer Indicating Transmitter
AIC-102	Instrumentation	Analyzer Indicating Controller
WT-101	Instrumentation	Weight Transmitter
WIC-101	Instrumentation	Weight Indicating Controller
LSH-103	Instrumentation	Level Switch High
LAH-103	Instrumentation	Level Alarm High
LSL-103	Instrumentation	Level Switch Low
LAL-103	Instrumentation	Level Alarm Low
LT-103	Instrumentation	Level Transmitter
LIC-103	Instrumentation	Level Indicating Controller
UY-101	Instrumentation	Signal Converter / Relay
6"-CS150-BAU-1001	Piping	Bauxite Feed Line
6"-CS150-BAU-1002	Piping	Bauxite Gravity Feed Line
6"-CS150-BAU-1003	Piping	Crushed Bauxite Line
6"-CS150-BAU-1004	Piping	Conveyor Discharge Line
6"-CS150-BAU-1005	Piping	Day Bin Discharge Line

- General Notes**
- All pipes, fittings, and valves shall be designed in accordance with ASME B31.3 process piping standards.
 - All instrumentation symbols and nomenclature conform to ISA 5.1 standards. Fail-safe actions for all pneumatic control valves (fail-open/fail-closed) shall be determined during the HAZOP review phase.
 - All gravity chutes and hoppers handling solid bauxite shall be lined with abrasion-resistant plates to prevent wear.
 - Minimum incline angle for all solid-feed gravity chutes is 60 degrees to horizontal to prevent bridging and blockages.
 - All conveyor transfer points (FD-101, CV-101) require local exhaust ventilation (LEV) tie-ins to prevent fugitive dust emissions.

No.	Revision/Issue	Date

Drawing Name
Area 100
Raw Material
Handling & Primary
Communion

Project Name and Address
PAC_P&ID
Final Year Project
PMB, UPO, KNUST, Ghana
Kumasi Ashanti Region

Area	Sheet
100	
Drawing Number	
1	
Author	GROUP 7B