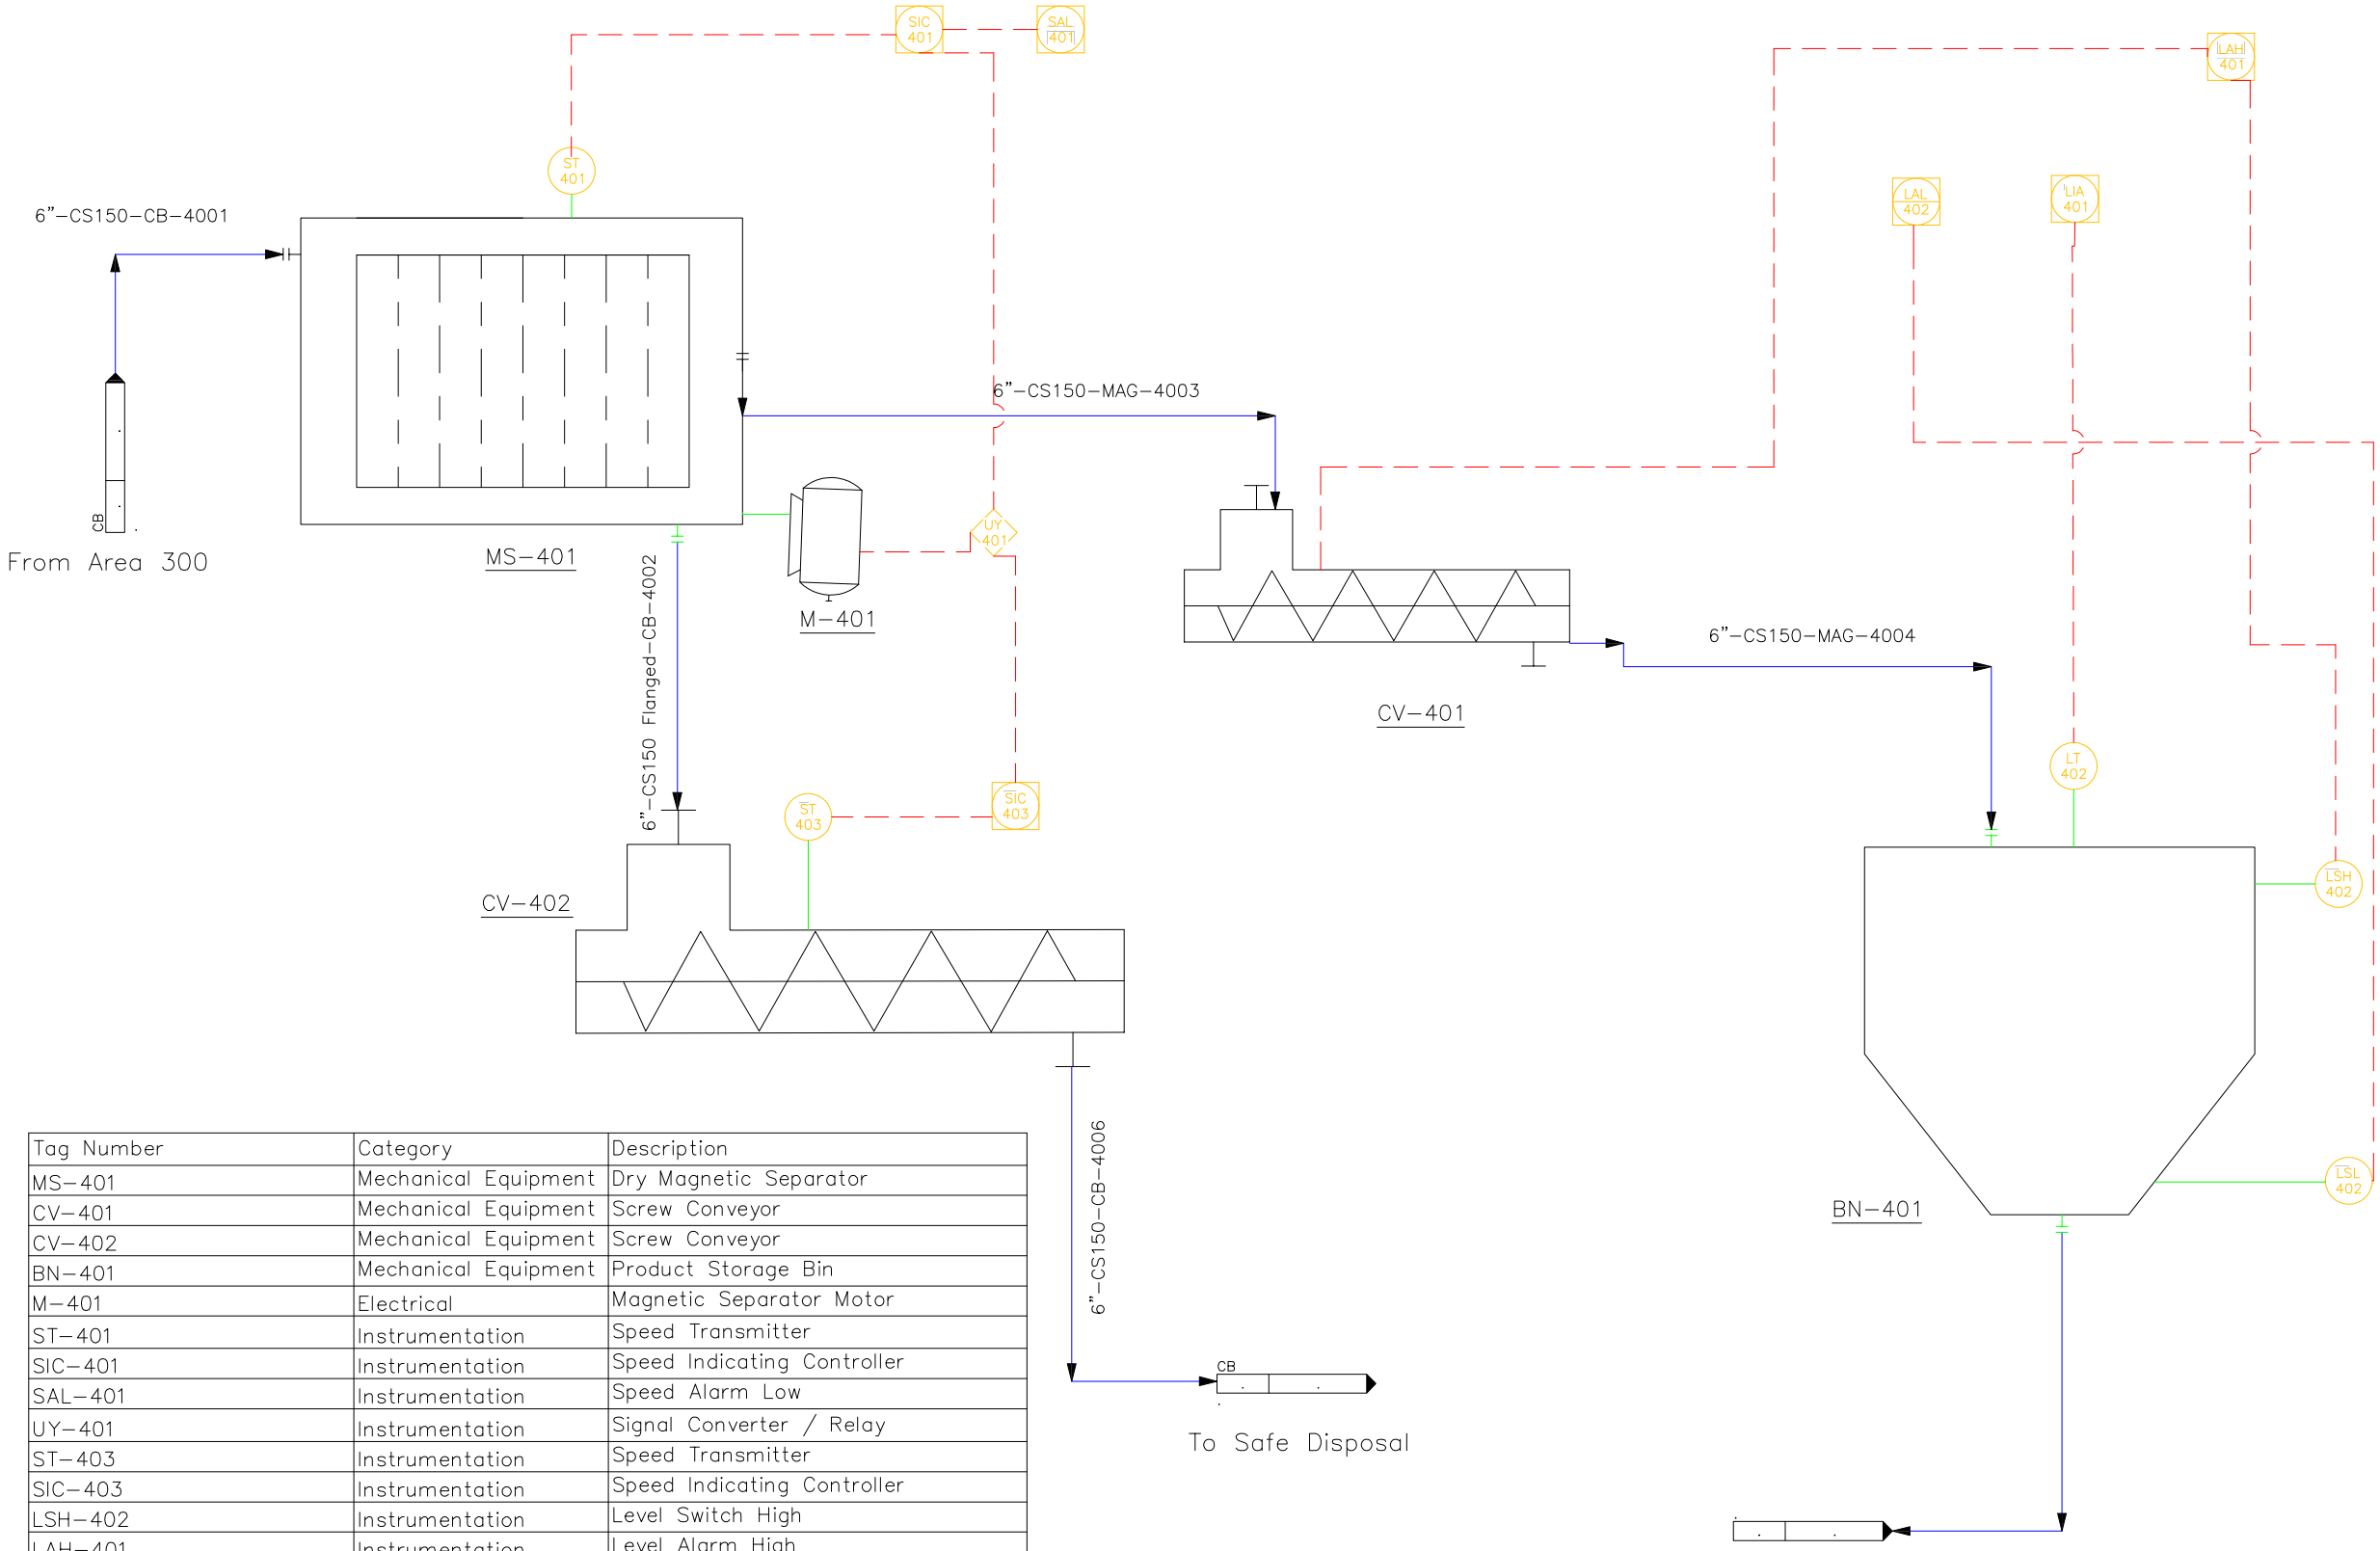


Tag Number	Category	Description
MS–401	Mechanical Equipment	Dry Magnetic Separator
CV–401	Mechanical Equipment	Screw Conveyor
CV–402	Mechanical Equipment	Screw Conveyor
BN–401	Mechanical Equipment	Product Storage Bin
M–401	Electrical	Magnetic Separator Motor
ST–401	Instrumentation	Speed Transmitter
SIC–401	Instrumentation	Speed Indicating Controller
SAL–401	Instrumentation	Speed Alarm Low
UY–401	Instrumentation	Signal Converter / Relay
ST–403	Instrumentation	Speed Transmitter
SIC–403	Instrumentation	Speed Indicating Controller
LSH–402	Instrumentation	Level Switch High
LAH–401	Instrumentation	Level Alarm High
LT–402	Instrumentation	Level Transmitter
LIA–401	Instrumentation	Level Indicator with Alarm
LSL–402	Instrumentation	Level Switch Low
LAL–402	Instrumentation	Level Alarm Low
6"–CS150–CB–4001	Piping	Calcined Bauxite Inlet Line
6"–CS150 Flanged–CB–4002	Piping	Magnetic Waste Line
6"–CS150–MAG–4003	Piping	Cleaned Bauxite Line
6"–CS150–MAG–4004	Piping	Cleaned Bauxite Conveyor Discharge
6"–CS150–CB–4006	Piping	Magnetic Waste Conveyor Discharge

General Notes

1. All pipes, fittings, and valves shall be designed in accordance with ASME B31.3 process piping standards.
2. All instrumentation symbols and nomenclature conform to ISA 5.1 standards.
3. Fail–safe actions for all pneumatic control valves (fail–open/fail–closed) shall be determined during the HAZOP review phase.
4. Electrical motors and instruments in this area must meet ATEX/IECEX rating for combustible dust environments.
5. Magnetic separator (MS–401) requires a dedicated maintenance clearance zone free of ferromagnetic structural steel.
6. All dry powder conveyors (CV–401, CV–402) and bins must be properly earthed to prevent static discharge.

No.	Revision/Issue	Date

Drawing Name
Area400
Dry Magnetic Separation

Project Name and Address
PAC_P&ID
Final Year Project
PMB, UPO, KNUST, Ghana
Kumasi Ashanti Region

Area	Stamp
400	
Drawing Number: 4	
Author: GROUP 7B	

C:\Users\psgya\OneDrive\Documents\PlantDesign\Drawings\PAC_P&ID\PID DWG\Area400.dwg